


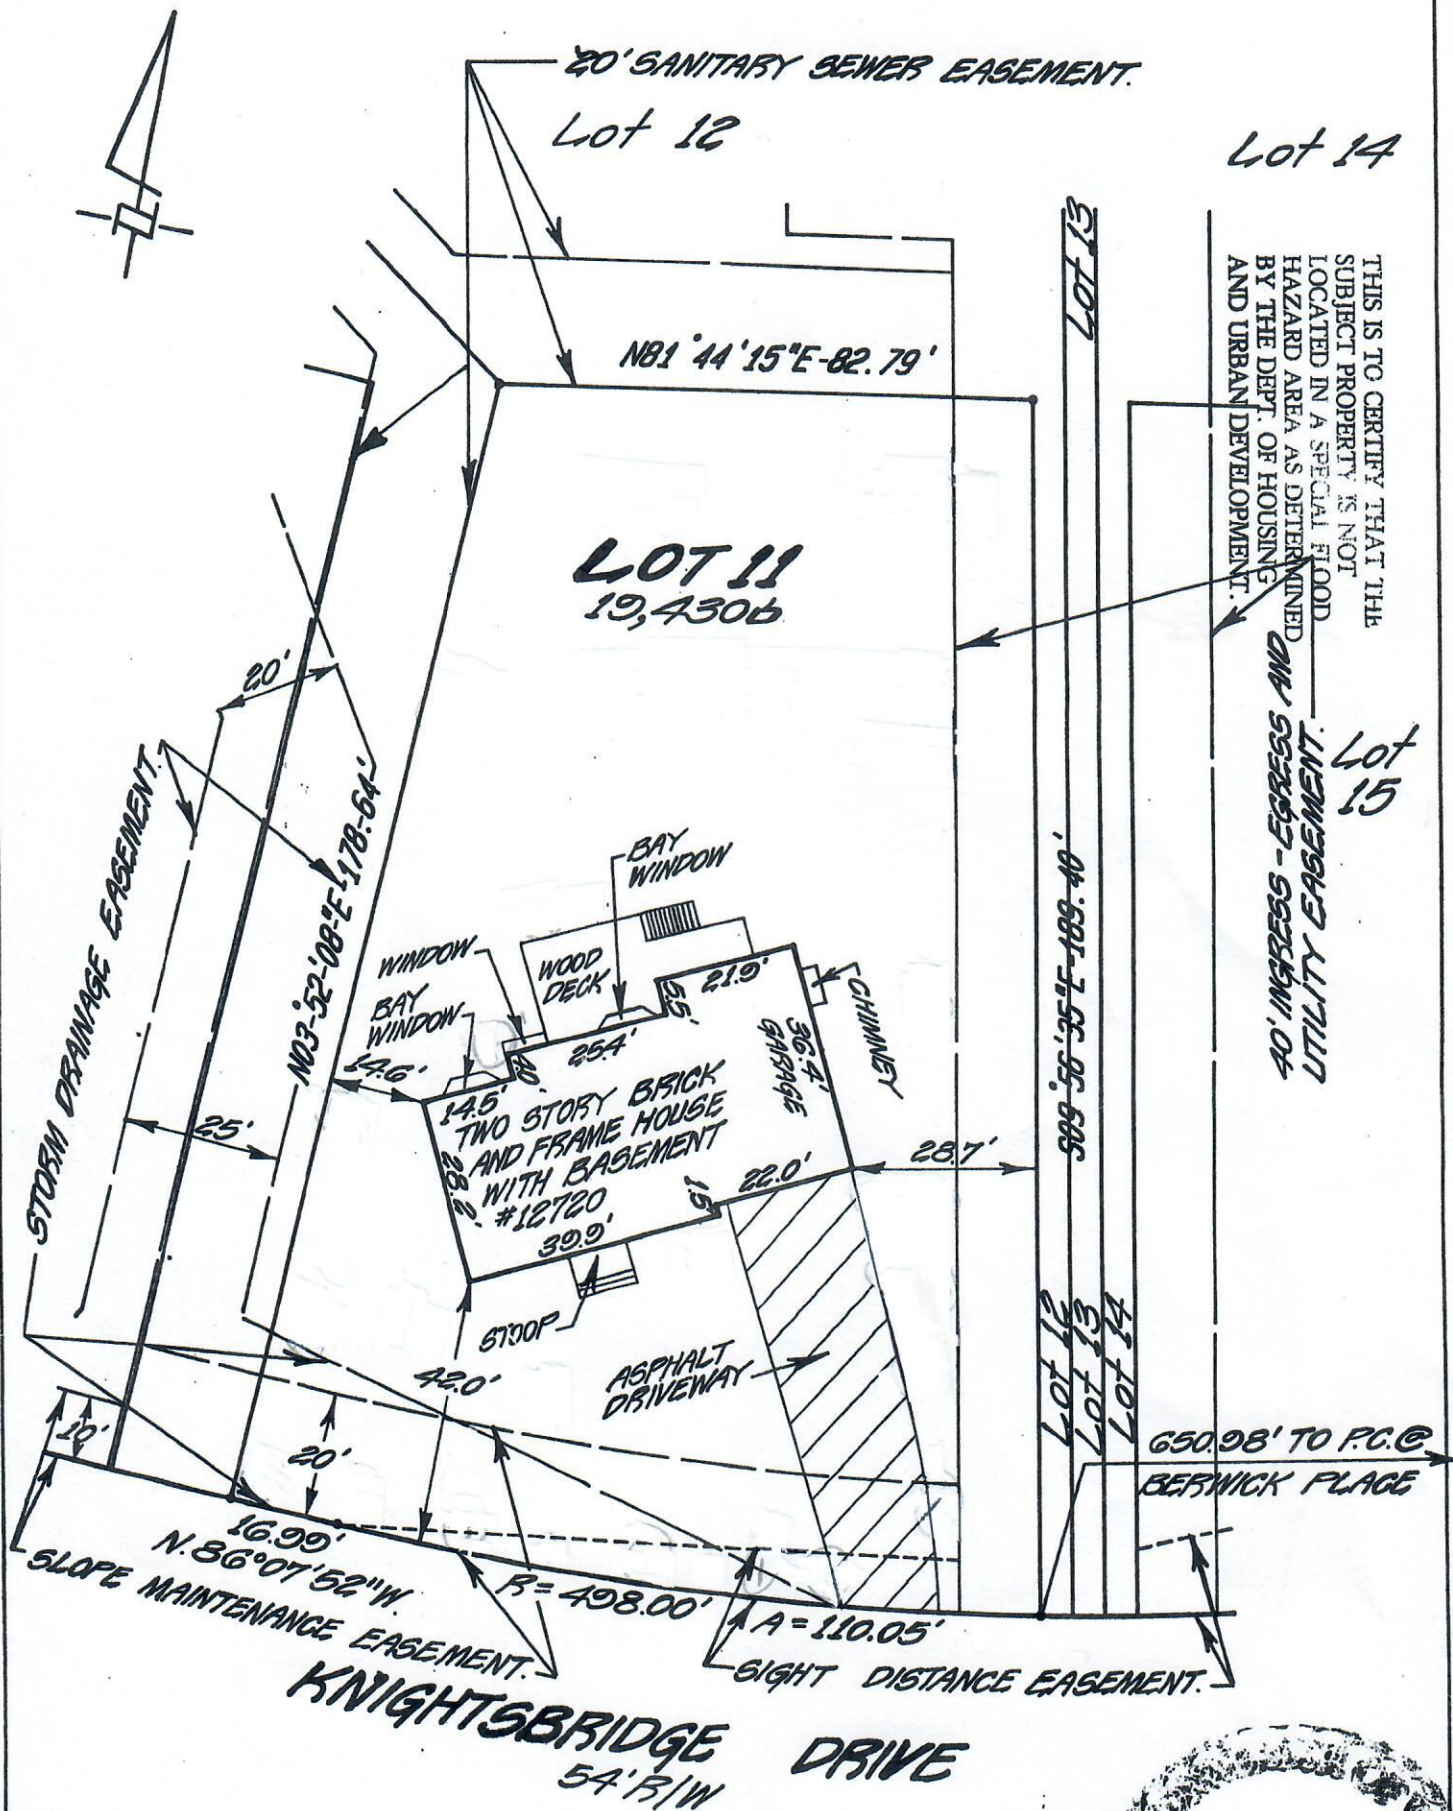

HOUSE LOCATION SURVEY

LOT 11 SECTION 6

LARRY M. SCARTZ
CERT. NO.